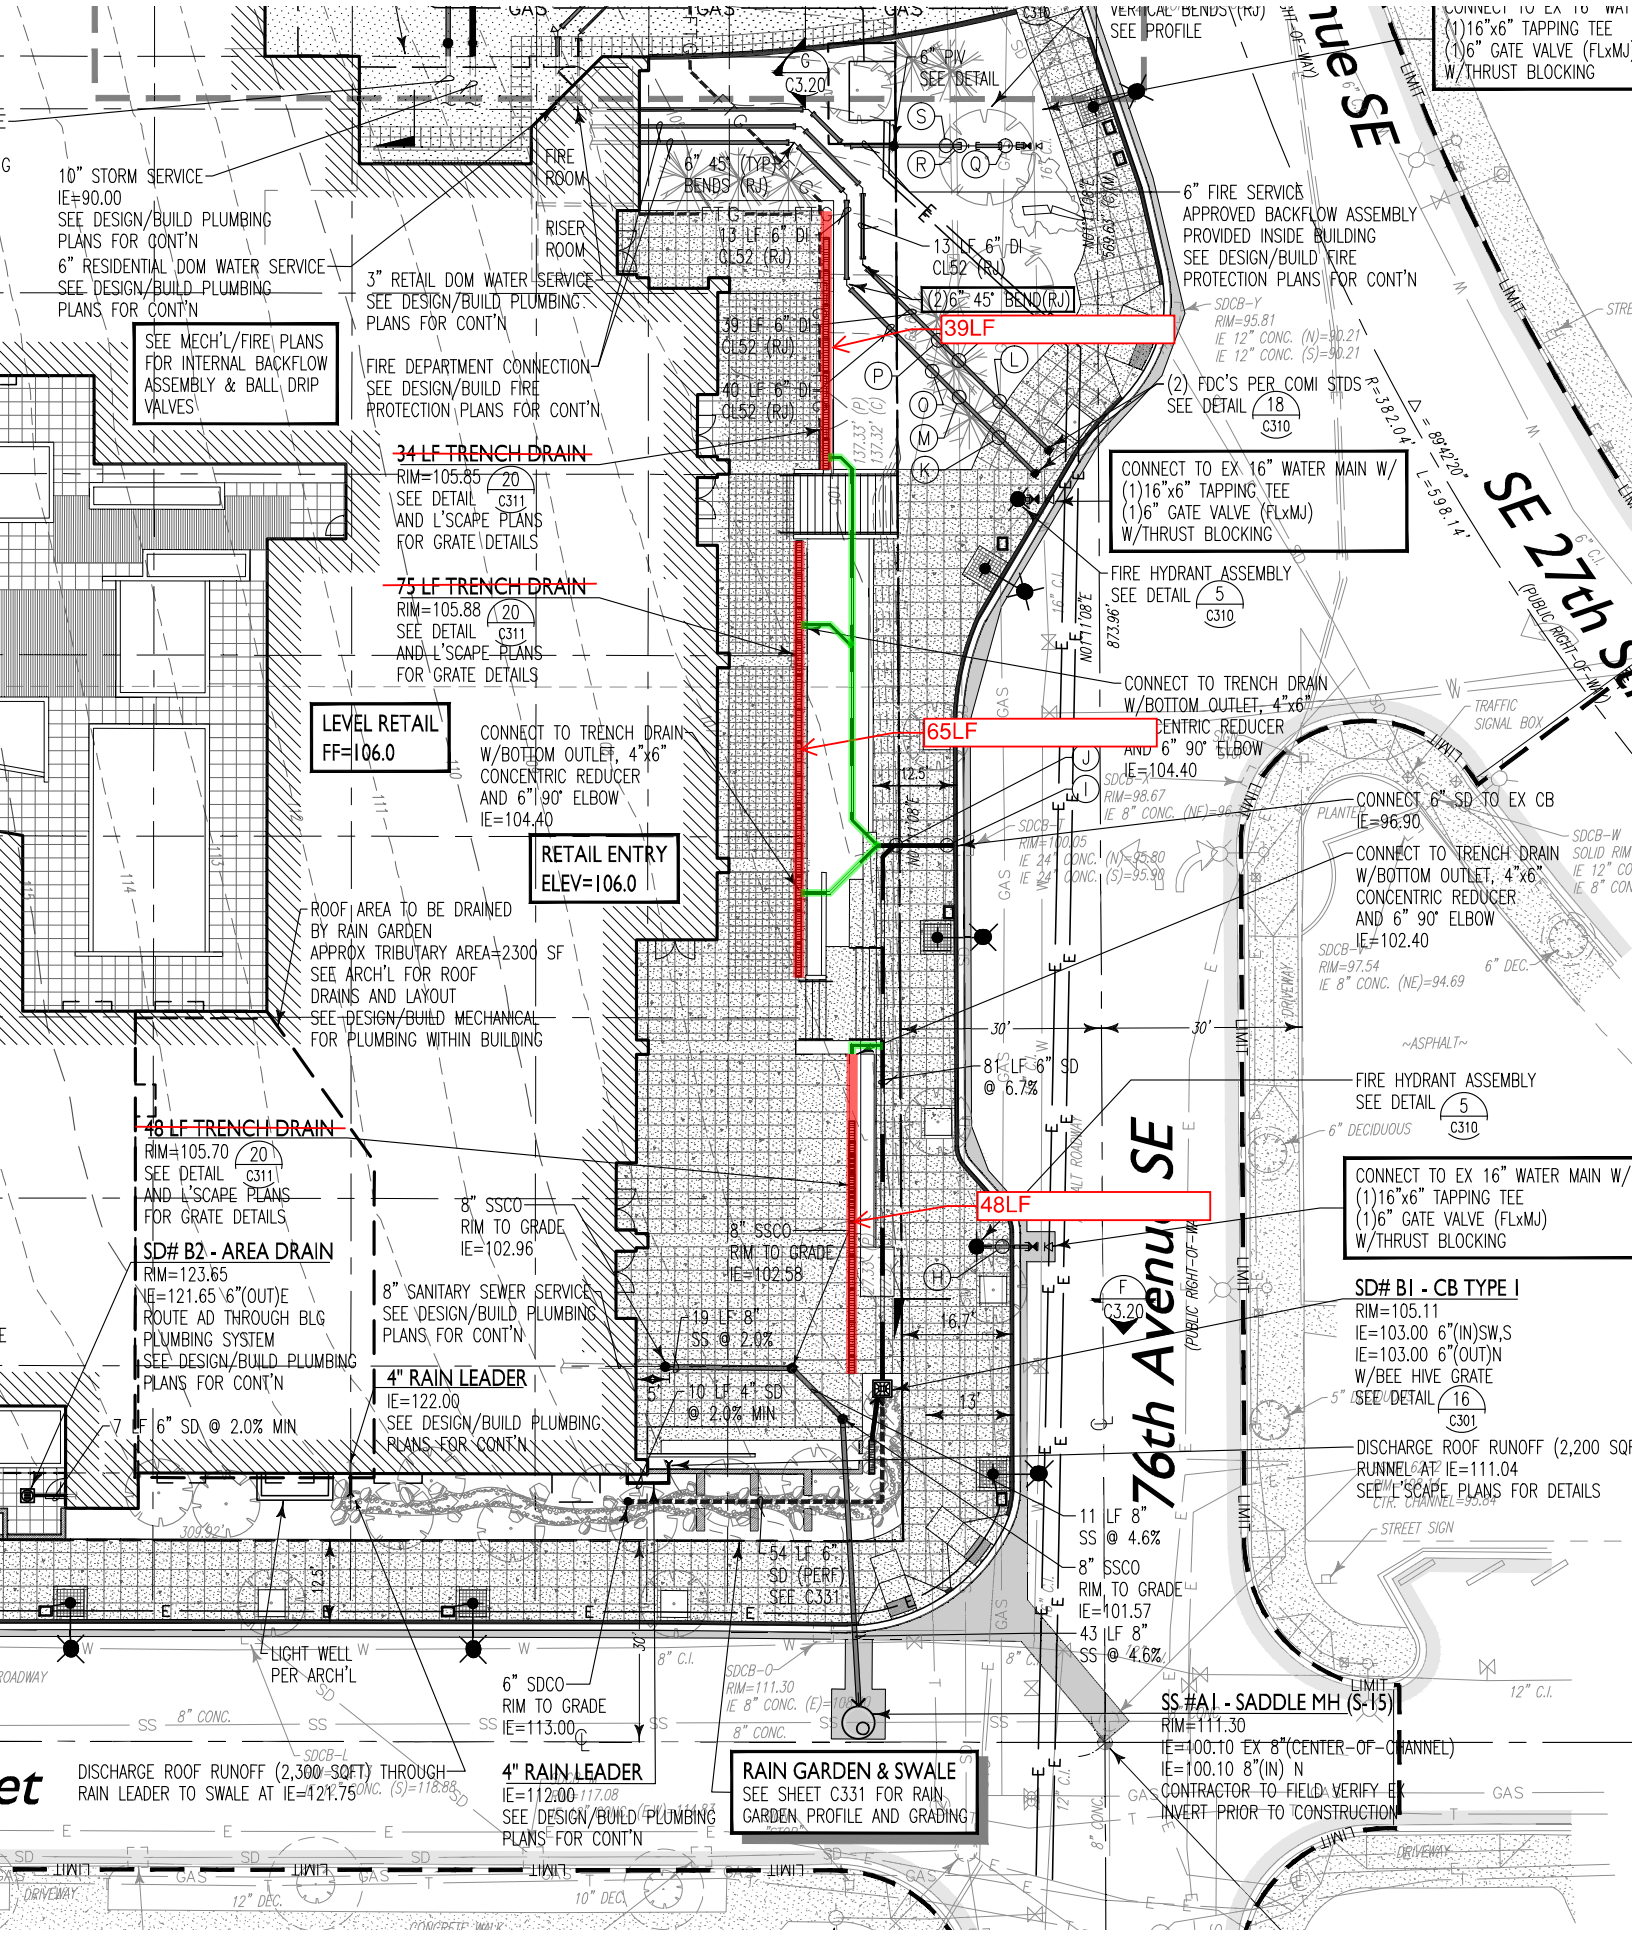
10" STORM SERVICE
IE=90.00
SEE DESIGN/BUILD PLUMBING
PLANS FOR CONT'N
6" RESIDENTIAL DOM WATER SERVICE
SEE DESIGN/BUILD PLUMBING
PLANS FOR CONT'N
SEE MECH'L/FIRE PLANS
FOR INTERNAL BACKFLOW
ASSEMBLY & BALL DRIP
VALVES
FIRE ROOM
RISER ROOM
3" RETAIL DOM WATER SERVICE
SEE DESIGN/BUILD PLUMBING
PLANS FOR CONT'N
FIRE DEPARTMENT CONNECTION
SEE DESIGN/BUILD FIRE
PROTECTION PLANS FOR CONT'N
6" 45° (TYP)
BENDS (RJ)
13 LF 6" DI
CL52 (RJ)
39 LF 6" DI
CL52 (RJ)
40 LF 6" DI
CL52 (RJ)
(2) 6" 45° BEND (RJ)
39LF
34 LF TRENCH DRAIN
RIM=105.85
SEE DETAIL 20 C311
AND L'SCAPE PLANS
FOR GRATE DETAILS
75 LF TRENCH DRAIN
RIM=105.88
SEE DETAIL 20 C311
AND L'SCAPE PLANS
FOR GRATE DETAILS
LEVEL RETAIL
FF=106.0
CONNECT TO TRENCH DRAIN
W/BOTTOM OUTLET, 4"x6"
CONCENTRIC REDUCER
AND 6" 90° ELBOW
IE=104.40
65LF
RETAIL ENTRY
ELEV=106.0
ROOF AREA TO BE DRAINED
BY RAIN GARDEN
APPROX TRIBUTARY AREA=2300 SF
SEE ARCH'L FOR ROOF
DRAINS AND LAYOUT
SEE DESIGN/BUILD MECHANICAL
FOR PLUMBING WITHIN BUILDING
48 LF TRENCH DRAIN
RIM=105.70
SEE DETAIL 20 C311
AND L'SCAPE PLANS
FOR GRATE DETAILS
48LF
SD# B2 - AREA DRAIN
RIM=123.65
IE=121.65 6"(OUT)E
ROUTE AD THROUGH BLG
PLUMBING SYSTEM
SEE DESIGN/BUILD PLUMBING
PLANS FOR CONT'N
8" SSCO
RIM TO GRADE
IE=102.96
8" SSCO
RIM TO GRADE
IE=102.58
8" SANITARY SEWER SERVICE
SEE DESIGN/BUILD PLUMBING
PLANS FOR CONT'N
19 LF 8"
SS @ 2.0%
4" RAIN LEADER
IE=122.00
SEE DESIGN/BUILD PLUMBING
PLANS FOR CONT'N
7 LF 6" SD @ 2.0% MIN
10 LF 4" SD
@ 2.0% MIN
81 LF 6" SD
@ 6.7%
54 LF 6"
SD (PERF)
SEE C331
11 LF 8"
SS @ 4.6%
8" SSCO
RIM TO GRADE
IE=101.57
43 LF 8"
SS @ 4.6%
LIGHT WELL
PER ARCH'L
6" SDCO
RIM TO GRADE
IE=113.00
DISCHARGE ROOF RUNOFF (2,300 SQFT) THROUGH
RAIN LEADER TO SWALE AT IE=121.75
4" RAIN LEADER
IE=112.00
SEE DESIGN/BUILD PLUMBING
PLANS FOR CONT'N
RAIN GARDEN & SWALE
SEE SHEET C331 FOR RAIN
GARDEN PROFILE AND GRADING
6" PIV
SEE DETAIL
VERTICAL BENDS (RJ)
SEE PROFILE
6" FIRE SERVICE
APPROVED BACKFLOW ASSEMBLY
PROVIDED INSIDE BUILDING
SEE DESIGN/BUILD FIRE
PROTECTION PLANS FOR CONT'N
(2) FDC'S PER COMI STDS
SEE DETAIL 18 C310
CONNECT TO EX 16" WATER MAIN W/
(1)16"x6" TAPPING TEE
(1)6" GATE VALVE (FLxMJ)
W/THRUST BLOCKING
FIRE HYDRANT ASSEMBLY
SEE DETAIL 5 C310
CONNECT TO TRENCH DRAIN
W/BOTTOM OUTLET, 4"x6"
CONCENTRIC REDUCER
AND 6" 90° ELBOW
IE=104.40
CONNECT 6" SD TO EX CB
IE=96.90
CONNECT TO TRENCH DRAIN
W/BOTTOM OUTLET, 4"x6"
CONCENTRIC REDUCER
AND 6" 90° ELBOW
IE=102.40
FIRE HYDRANT ASSEMBLY
SEE DETAIL 5 C310
CONNECT TO EX 16" WATER MAIN W/
(1)16"x6" TAPPING TEE
(1)6" GATE VALVE (FLxMJ)
W/THRUST BLOCKING
SD# B1 - CB TYPE I
RIM=105.11
IE=103.00 6"(IN)SW,S
IE=103.00 6"(OUT)N
W/BEE HIVE GRATE
SEE DETAIL 16 C301
DISCHARGE ROOF RUNOFF (2,200 SQF
RUNNEL AT IE=111.04
SEE L'SCAPE PLANS FOR DETAILS
SS #A1 - SADDLE MH (S-15)
RIM=111.30
IE=100.10 EX 8"(CENTER-OF-CHANNEL)
IE=100.10 8"(IN) N
CONTRACTOR TO FIELD VERIFY EX
INVERT PRIOR TO CONSTRUCTION
76th Avenue SE
SE 27th St
~ASPHALT~
STREET SIGN
TRAFFIC SIGNAL BOX